CHURCH DEVELOPMENT BUILDING

FOR

INSIGHT CHRISTIAN ASSEMBLY. INT'L, INC.

AT

OGBOMO STREET,
OGUNMWENYIN ROAD,
OREDO LOCAL GOVT. AREA
EDO STATE.

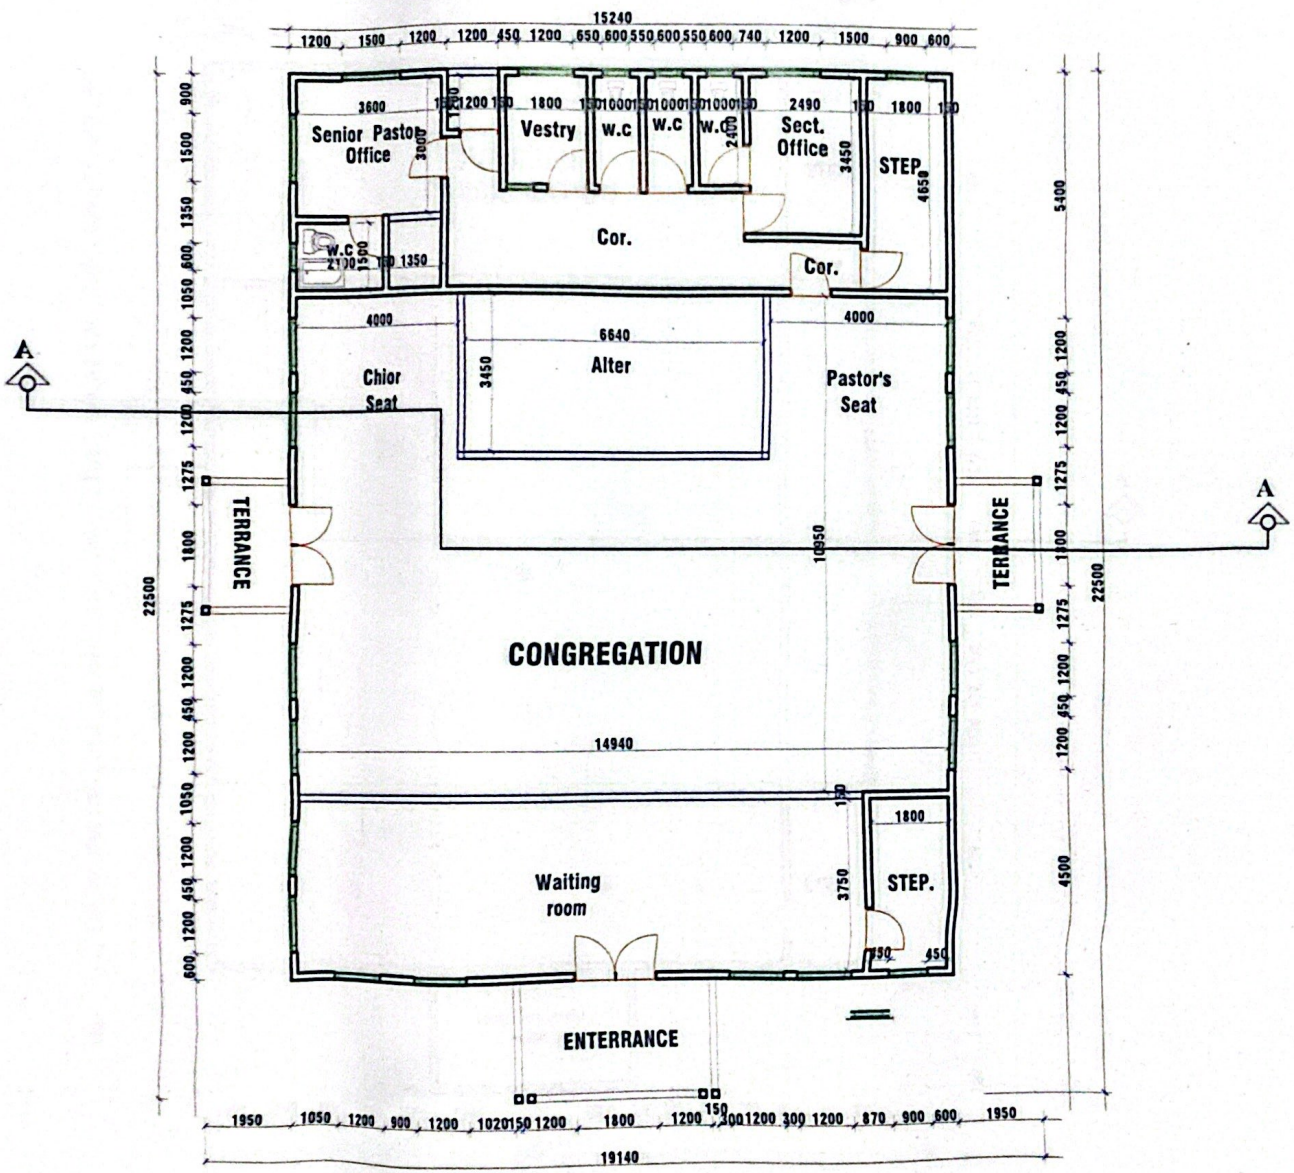

GRD. FLOOR PLAN

Office Use

Note Revisions / Issue Date

Client
INSIGHT CHRISTIAN ASSEMBLY. INT'L, INC.

Project Title / Site
Church dev. building
@
Ogbomo Street, Ogunmwenyin Road.
Oredo Loc. Govt Area.
EDO STATE.

Drwg Title
GROUND FLOOR PLAN.

Design by -

Drawn by -

Checked Stamp & Sign by

Scale 1:100

Date

Drwg no

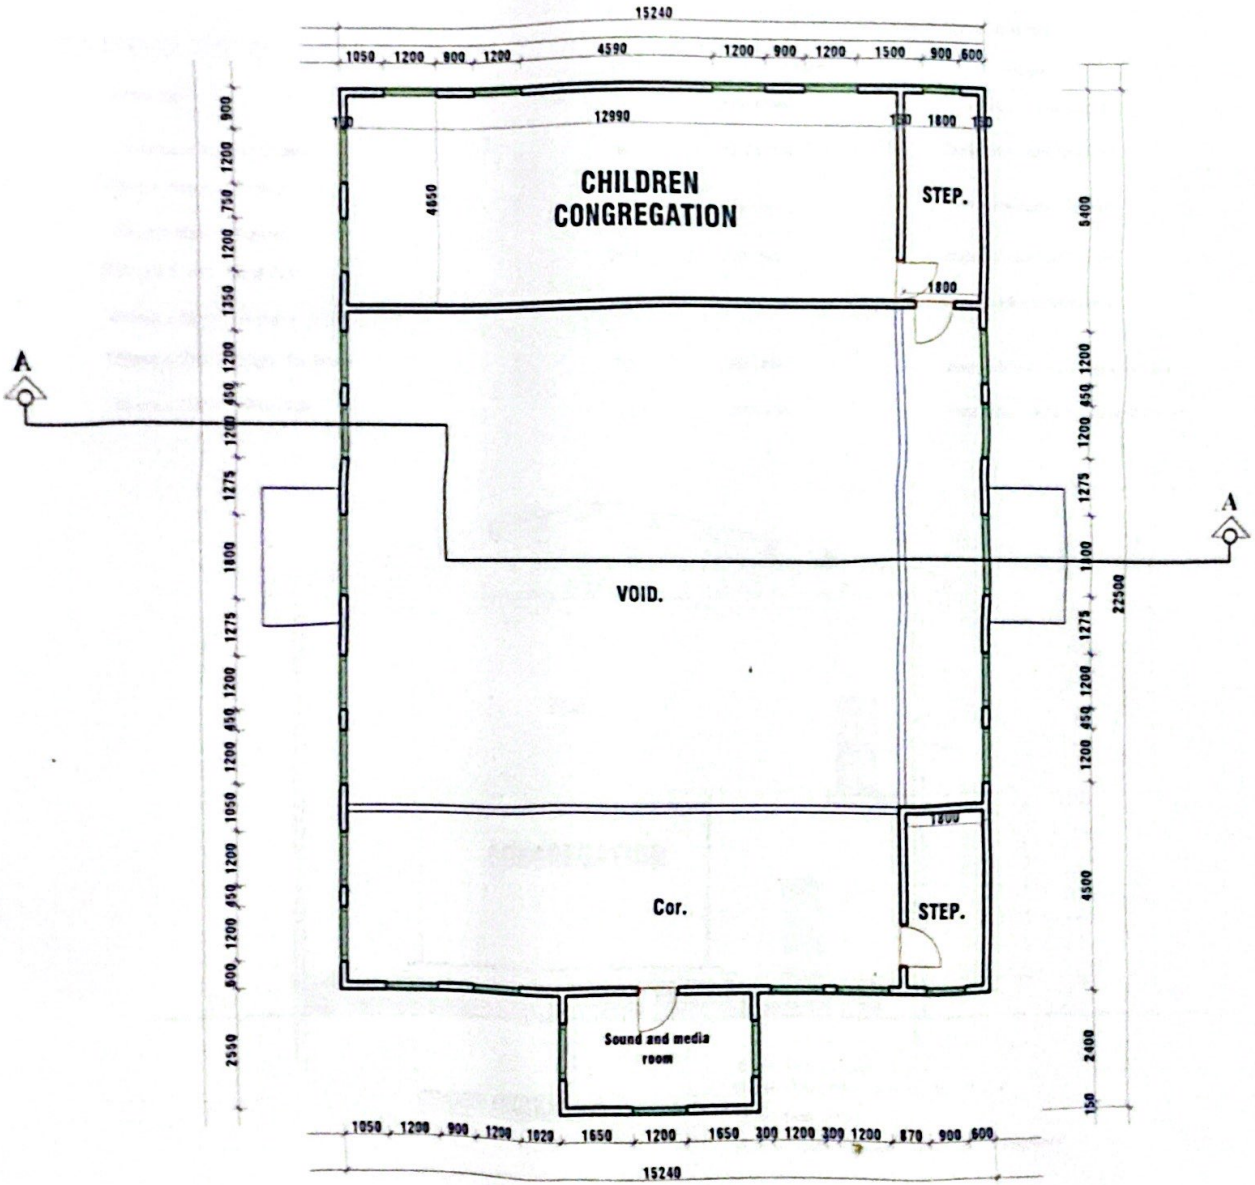

FIRST FLOOR PLAN

Office Use

Notes Revisions / Issue Date

Client
INSIGHT CHRISTIAN ASSEMBLY. INT'L. INC.

Project Title / Site
Church dev. building
@
Ogbomo Street, Ogunmwonyin Street,
Oredo Loc. Govt Area.
EDO STATE.

Drg. Title
FIRST FLOOR PLAN.

Design by -

Drawn by -

Checked, Stamp & Sign by

Scale 1:100

ROOF & CEILING MEMBERS

Ridge cap

Aluminium Roofing Sheet

75mm x 50mm Purlins

100mm x 50mm Rafters

100mm x 50mm King Post

100mm x 50mm Wooden Structs

150mm x 50mm Cross Tie Beam

100mm x 75mm Wall Plate

Windows & Doors Schedule

Types	Size	Remark
W 1	1800 x 1200	Triple Slide Aluminium Window
W 2	1200 x 1200	Double Slide Aluminium Window
W 3	900 x 900	Projected Aluminium Window
W 4	600 x 600	Projected Aluminium Window
D1	2400 x 2100	Double Slide Aluminium Door
D2	900 x 2100	45mm solid core panel hard wood door
D3	750 x 2100	45mm solid core panel hard wood door

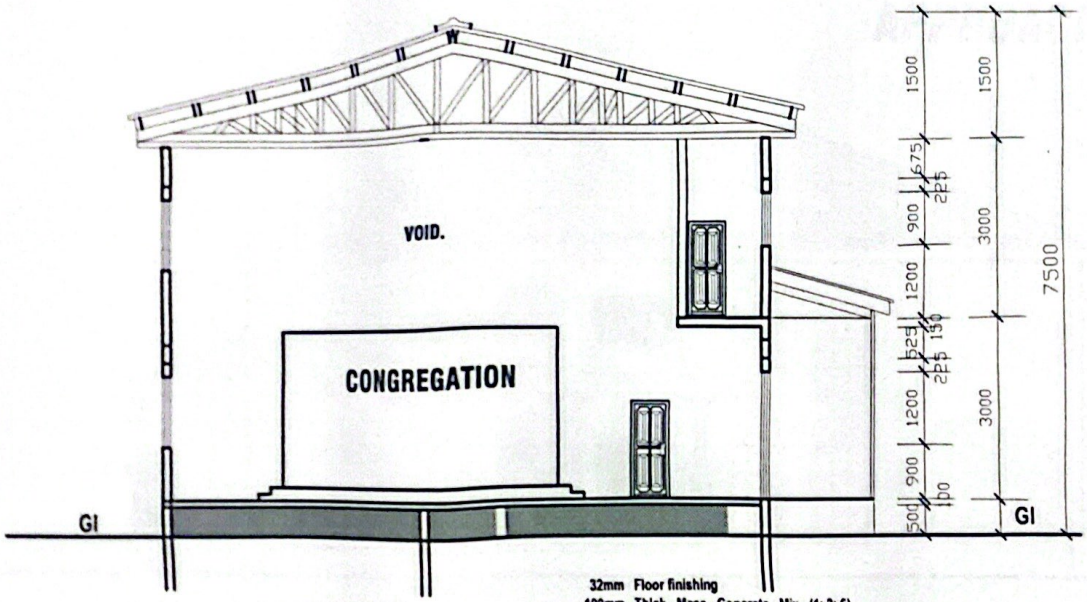

CROSS SECTION A-A

32mm Floor finishing
100mm Thick Mass Concrete Mix (1: 3: 6)
300mm Earth Filling
depth of foundation TO Be Determind by The Engineer's

Office Use

Note | Revisions / Issue

Client
INSIGHT CHRISTIAN ASSEMBLY. INT'L, INC.

Project Title / Site
Church dev. building
@
Ogbomo Street, Ogunmwanyin Road,
Oredo Loc. Govt Area.
EDO STATE.

Drwg Title
SECTION PLAN.

Design by -

Drawn by -

Checked Stamp & Sign by

Scale 1: 100

Date

Drwg No

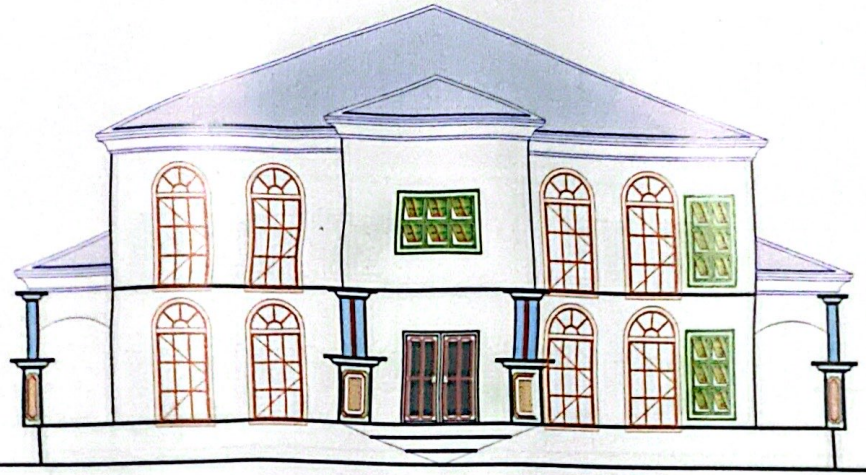

APPROACH VIEW

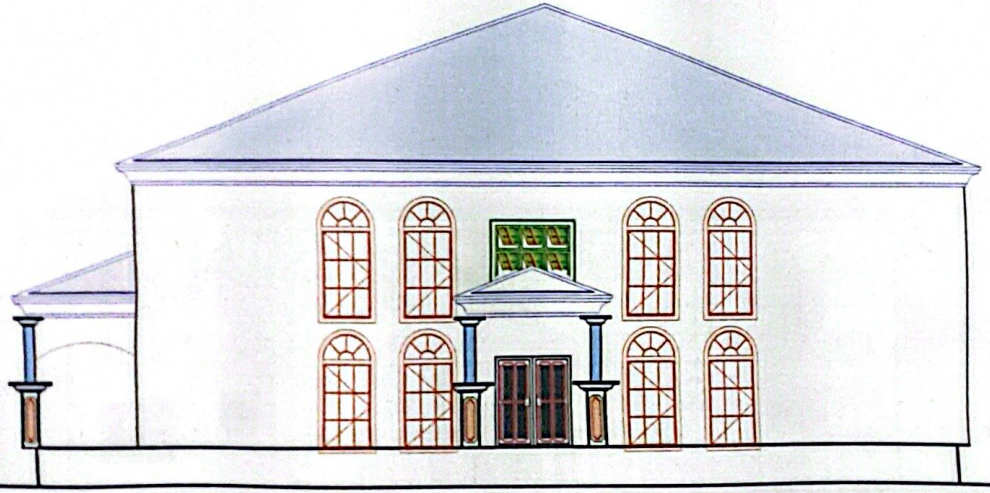

RIGHT SIDE VIEW

Office Use

Note	Revisions / Issue	Date

Client

INSIGHT CHRISTIAN ASSEMBLY. INT'L, INC.

Project Title / Site

Church dev. building
@
Ogbomo Street, Ogunmwenyin Road.
Oredo Loc. Govt Area.
EDO STATE.

Drwg Title

ELEVATIONS PLAN.

Design by -

Drawn by -

Checked Stamp & Sign by

Scale 1:100

Drwg no.

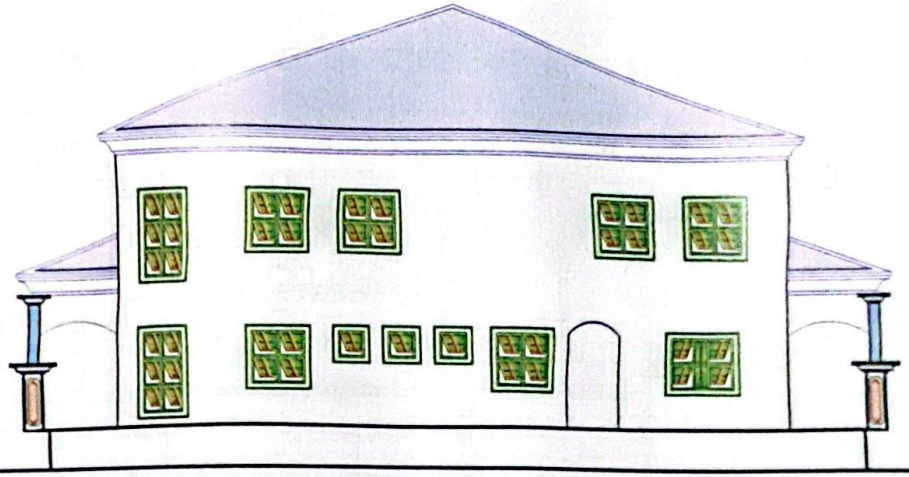

REAR VIEW

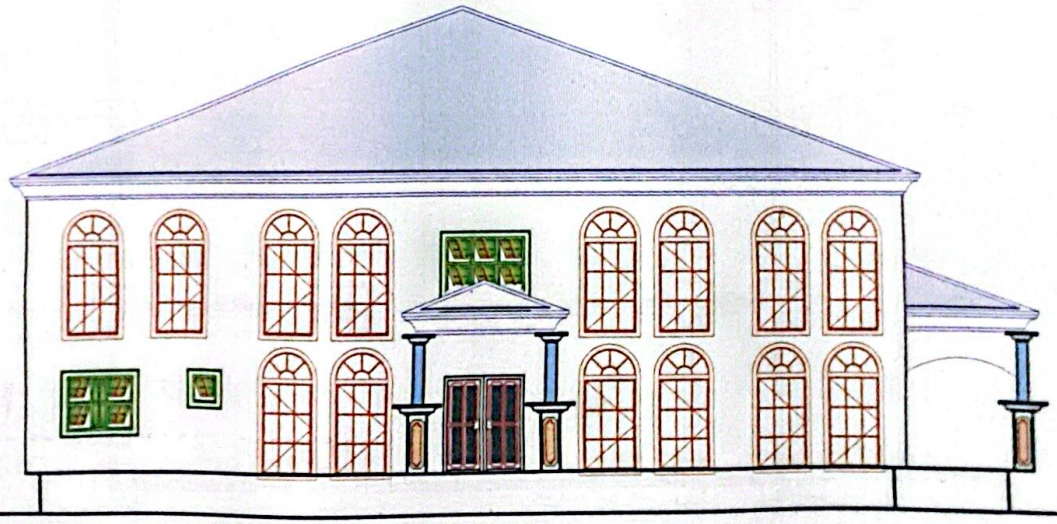

LEFT SIDE VIEW

Office Use

Note/ Revisions / Issue Date

Client

INSIGHT CHRISTIAN ASSEMBLY. INT'L, INC.

Project Title / Site

Church dev. building
@
Ogbomo Street, Ogunmwanyin Road,
Oredo Loc. Govt Area.
EDO STATE.

Drwg Title

ELEVATIONS PLAN.

Design by

Drawn by

Checked Stamp & Sign By

Scale 1:200

Drwg No

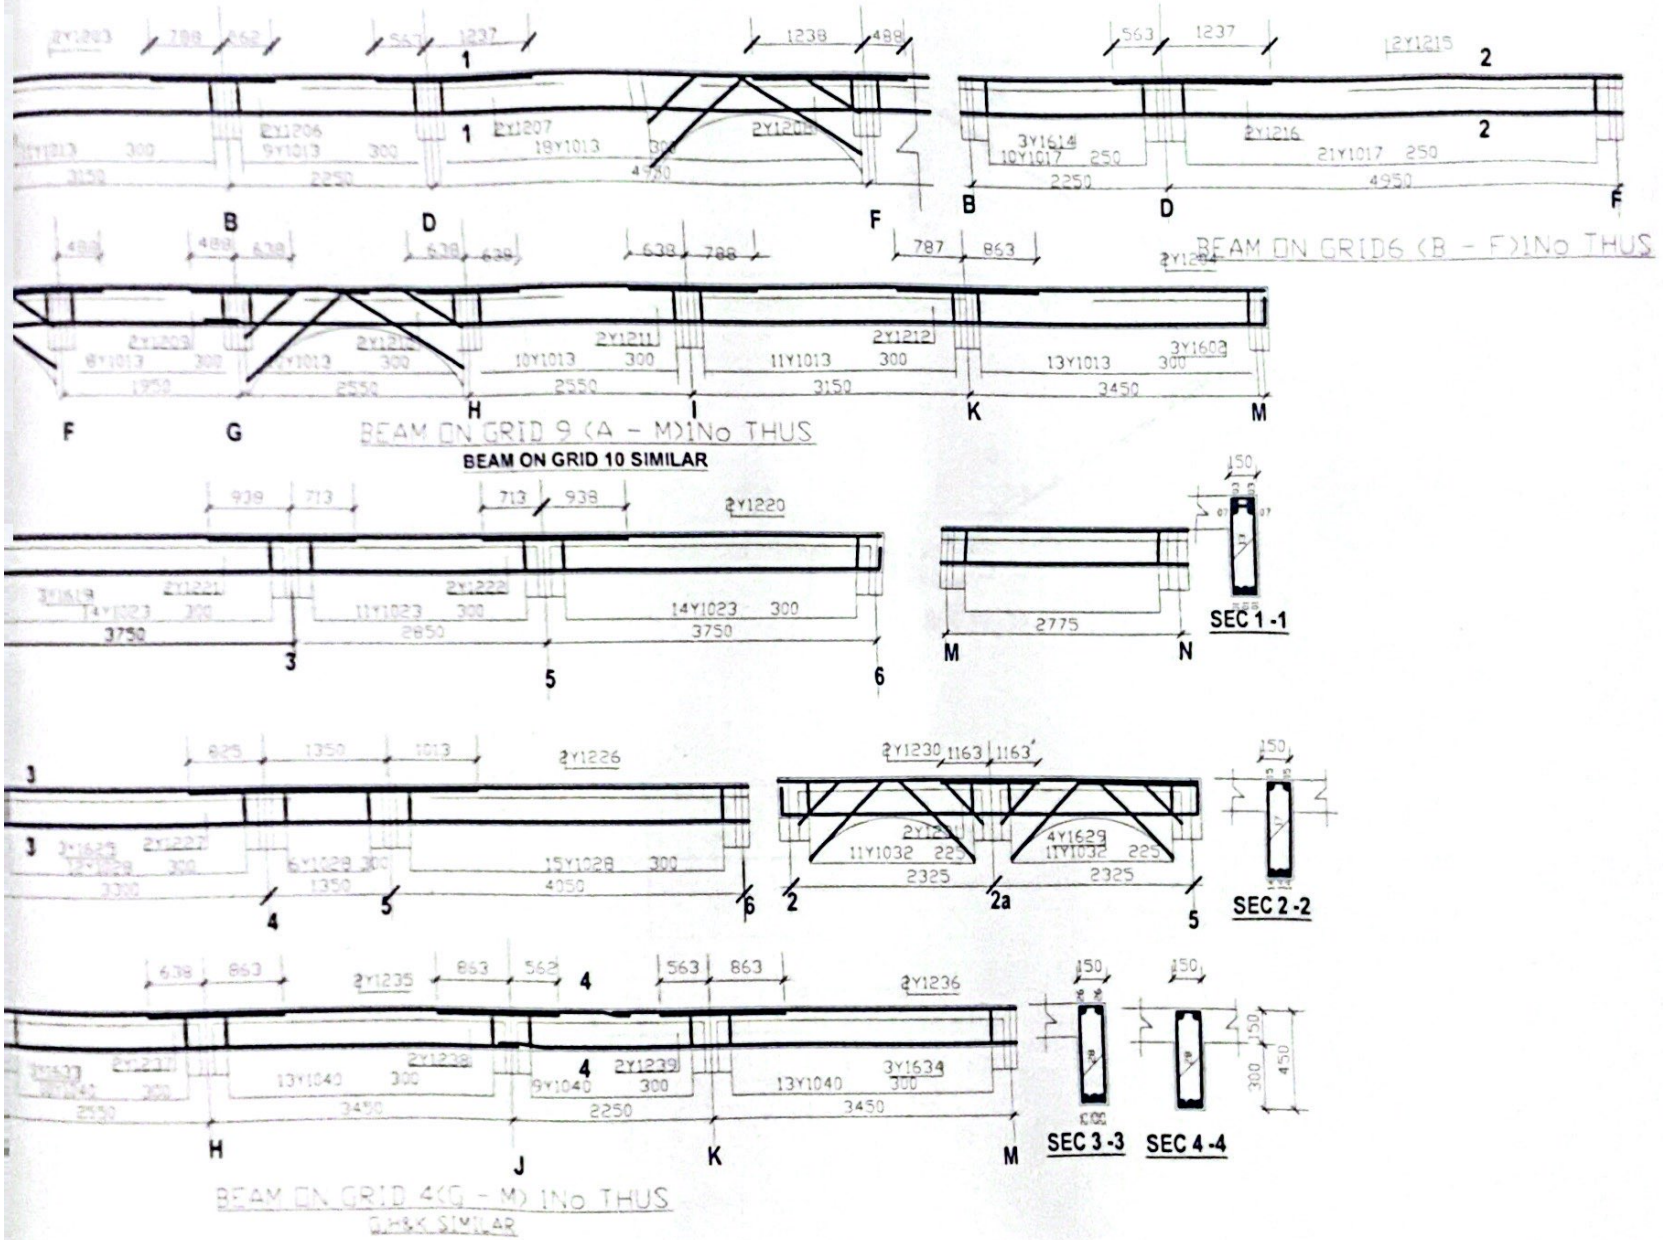

Office Use

Note Revisions / Issue Date

Client

INSIGHT CHRISTIAN ASSEMBLY. INT'L. INC.

Project Title / Site

Church dev. building
@
Ogbomo Street, Ogunmwonyin Road,
Oredo Loc. Govt Area.
EDO STATE.

Drwg. Title

BEAMS DETAILS.

Design by -

Drawn by -

Checked Stamp & Sign no

Scale 1:100

Date

Drwg no

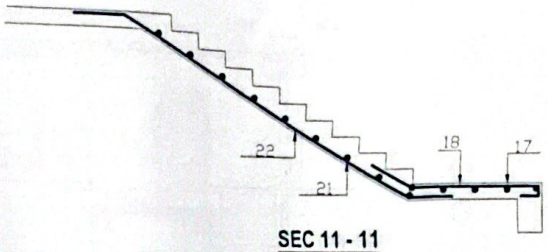

SEC 11 - 11

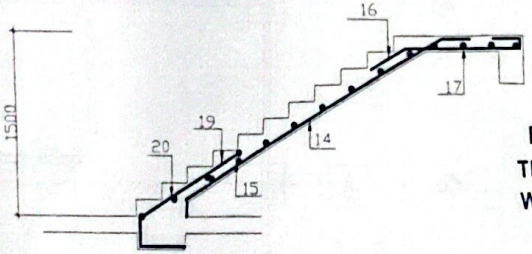

SEC 10 - 10

RISER	150
TREAD	300
WAIST	150

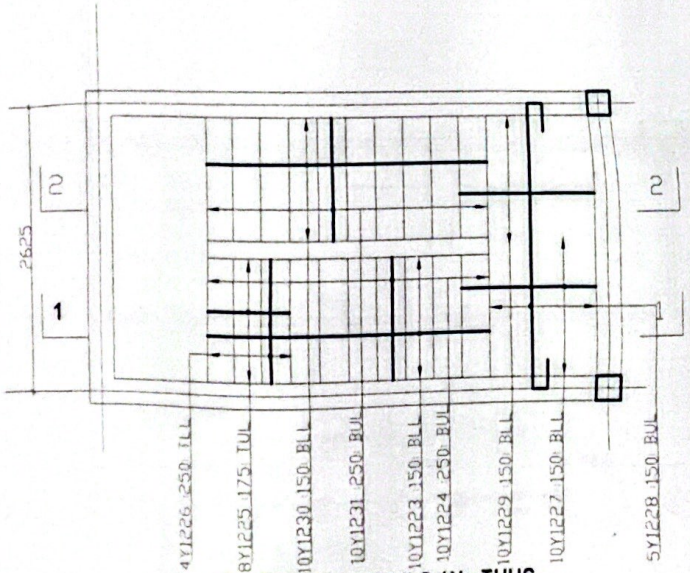

STAIR CASE DETAILS 1No THUS

Office Use

Note	Revisions / Issue	Date

Client

INSIGHT CHRISTIAN ASSEMBLY. INT'L, INC.

Project Title / Site.

Church dev. building
@
Ogbomo Street, Ogunmwenyin Road.
Oredo Loc. Govt Area.
EDO STATE.

Drwg Title

STAIRCASE DETAILS

Design by -

Drawn by -

Checked Stamp & Sign by

Scale 1: 100

Date

Drwg no